



ELEVATION 4G

ELEVATION 4H

Elevations 4G – 4H – 1/100




TN 100.17

ELEVATION 2D

ELEVATION 2E

TN 100.45

Elevation 2D – 2E – 1/100

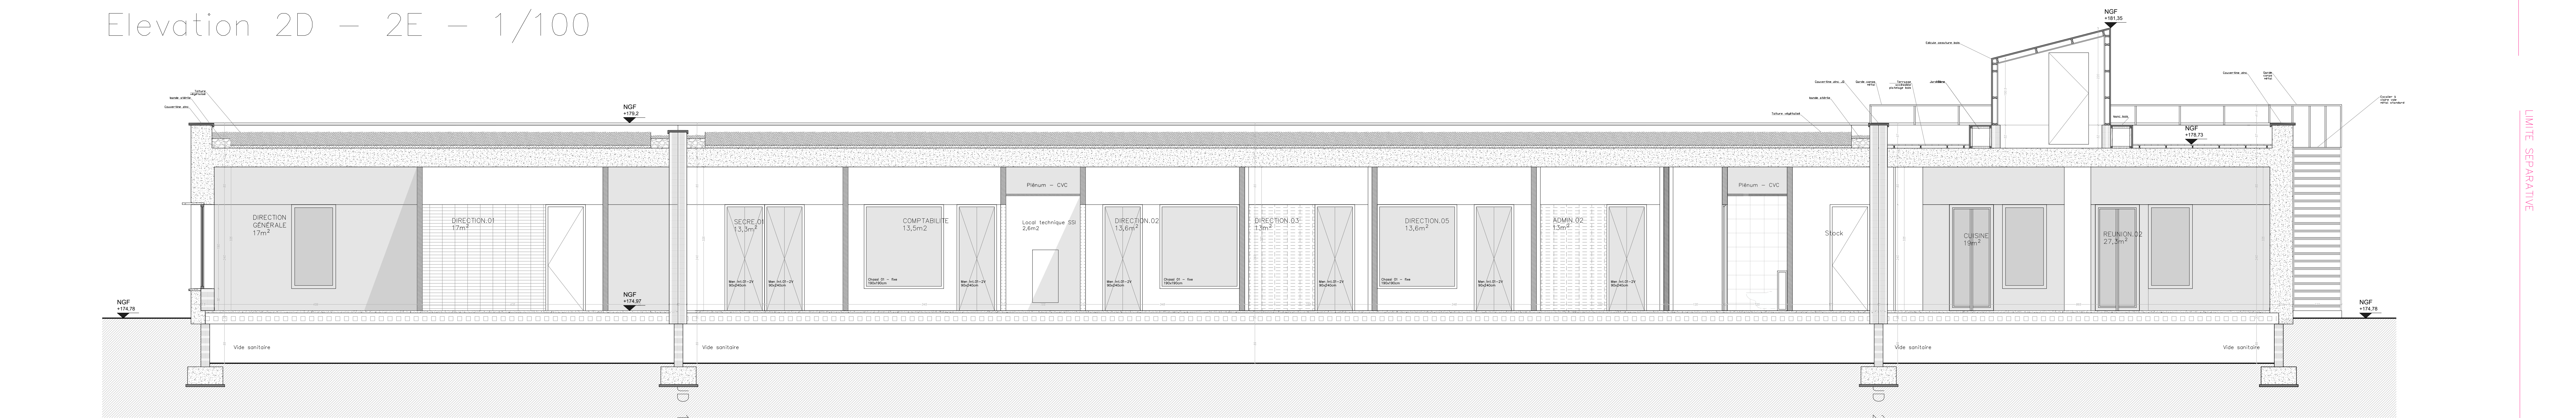

Coupe SS' – 1/100




ELEVATION 1A

ELEVATION 2A

ELEVATION 3A

Elevation 1A–2A–3A – 1/100

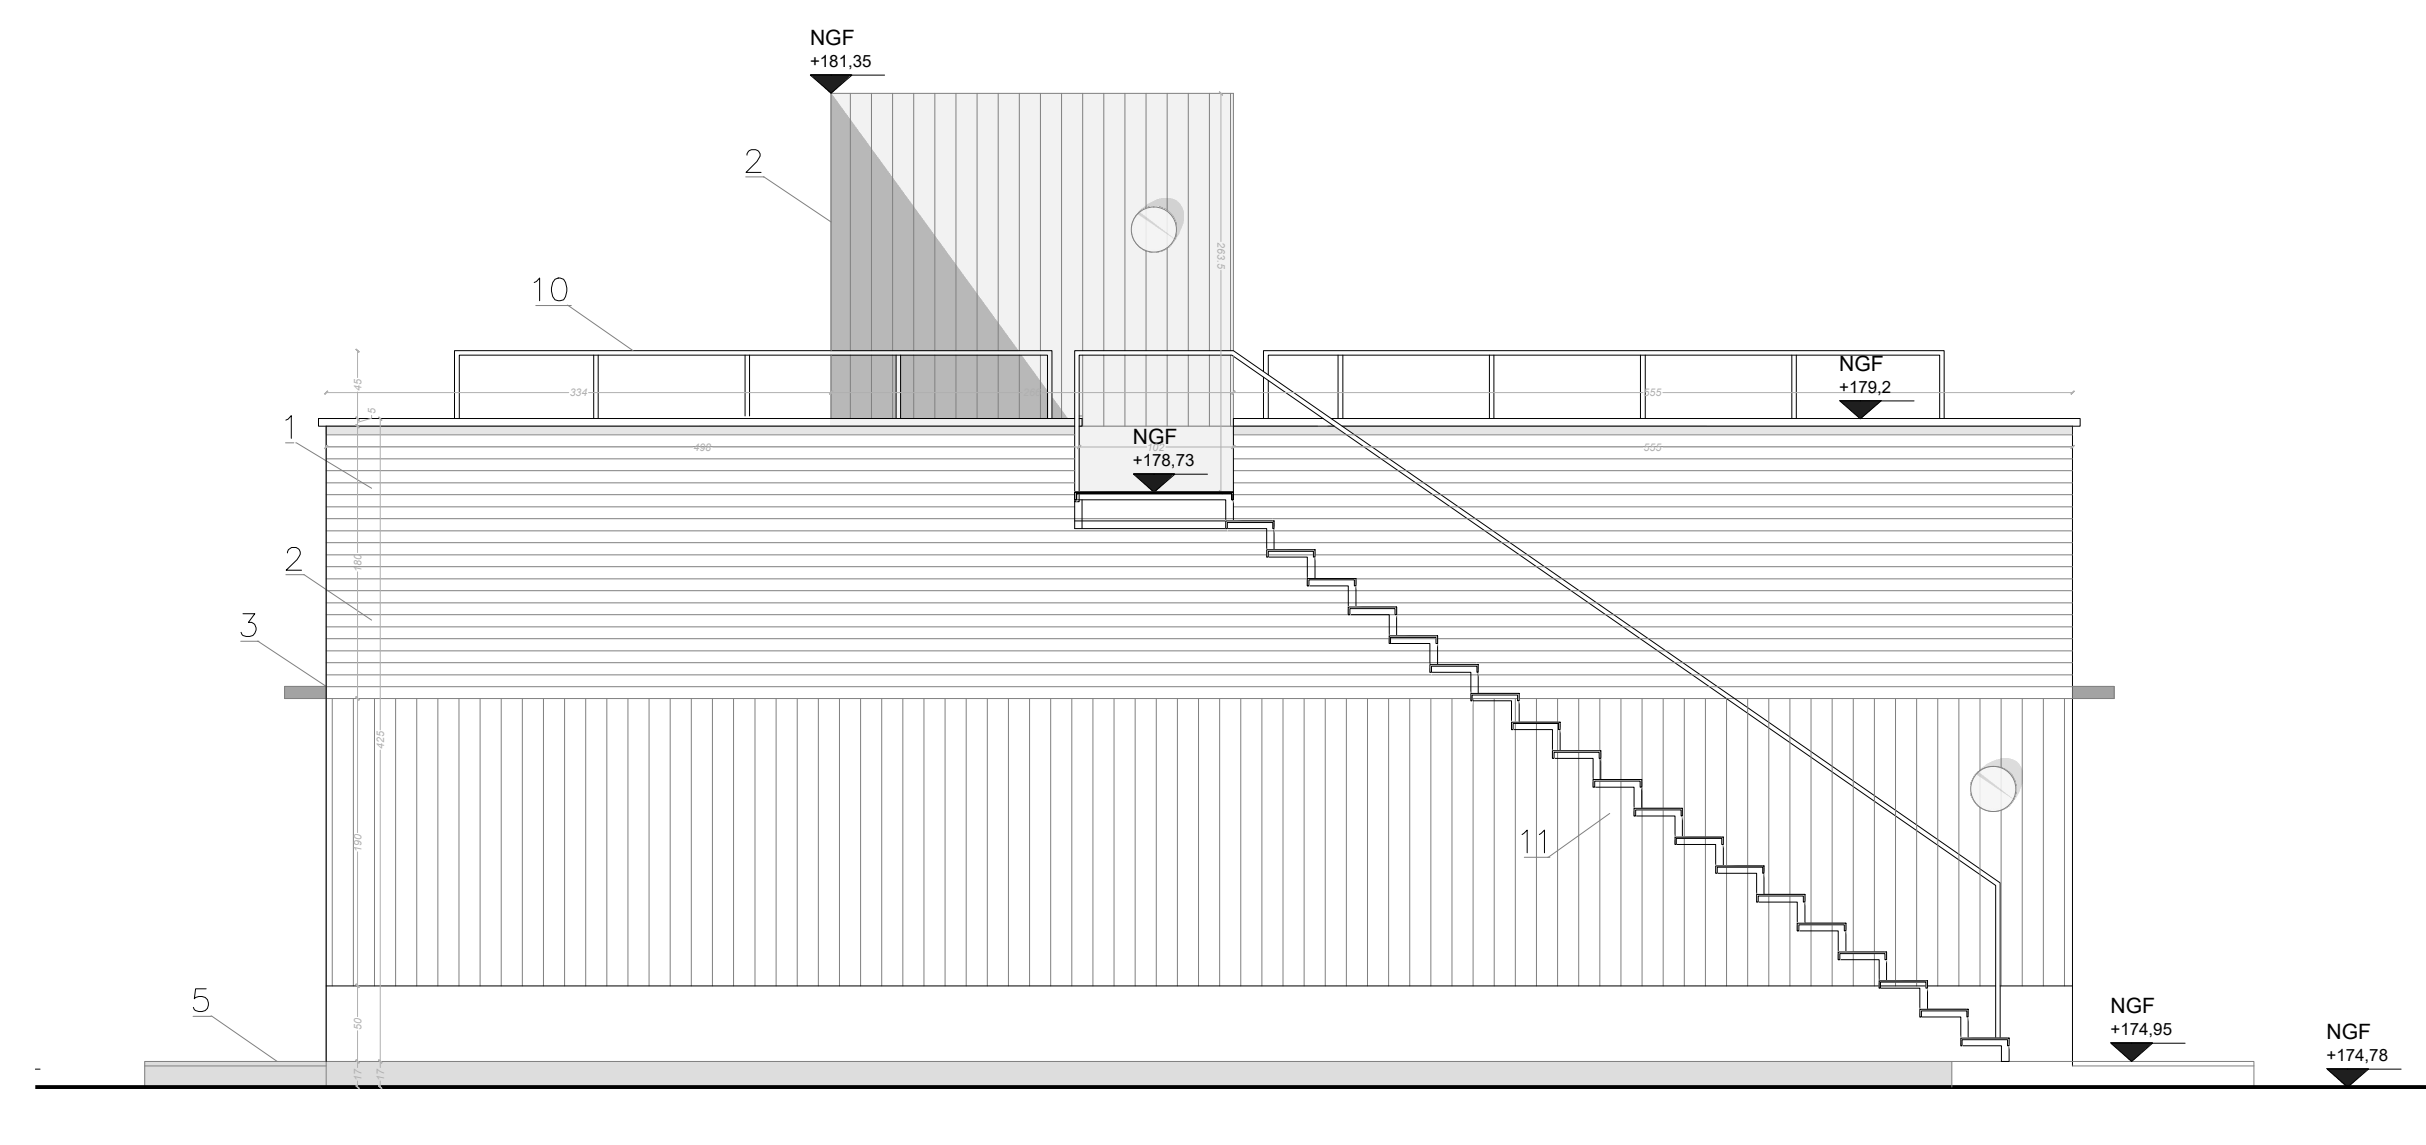

Elevation 3F – 1/100

MOE	MOA	PROJET	DOCUMENT	ECHELLE	LOT	FORMAT	DATE
MATHILDE LASSERRE – Architecte HMONP OÂ Ile-de-France – N°087975 63 Route de Rueil – 78150 – Le Chesnay lasserre.architecte@gmail.com +33680351075	ASSOCIATION LES TOUT PETITS Représentée par M.Legoff – Directeur Général 5 rue de Cernay – 91470 – Les Molières s.legoff@lestoutpetits.fr +33160121210	CONSTRUCTION DU SIEGE ADMINISTRATIF 1A allée de l'Orée du bois 91470 – Les Molières +33160121210	COUPE ET FACADES	1/50	----	A0	04/12/2024