


Coupe TT'

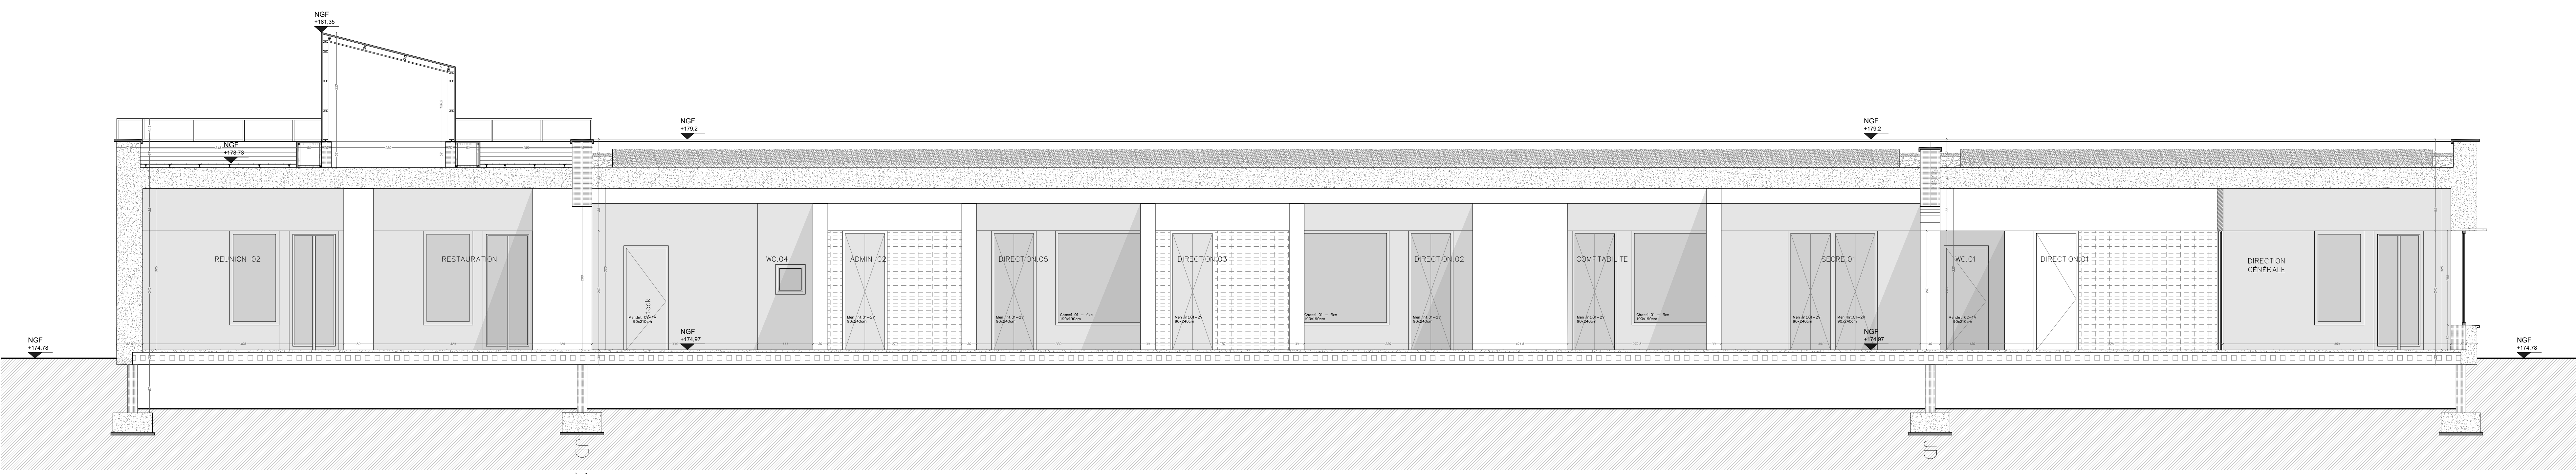

Coupe WW'

MOE	MOA	PROJET	DOCUMENT	ECHELLE	LOT	FORMAT	DATE
MATHILDE LASSERRE – Architecte HMONP OA Ile-de-France – N°087975 63 Route de Rueil – 78150 – Le Chesnay lasserre.architecte@gmail.com +33680351075	ASSOCIATION LES TOUT PETITS Représentée par M.Legoff – Directeur Général 5 rue de Cernay – 91470 – Les Molières s.legoff@lestoutpetits.fr +33160121210	CONSTRUCTION DU SIEGE ADMINISTRATIF 1A allée de l'Orée du bois 91470 – Les Molières +33160121210	COUPE LONGITUDINALE Est	1/50		A0	04/12/2024