




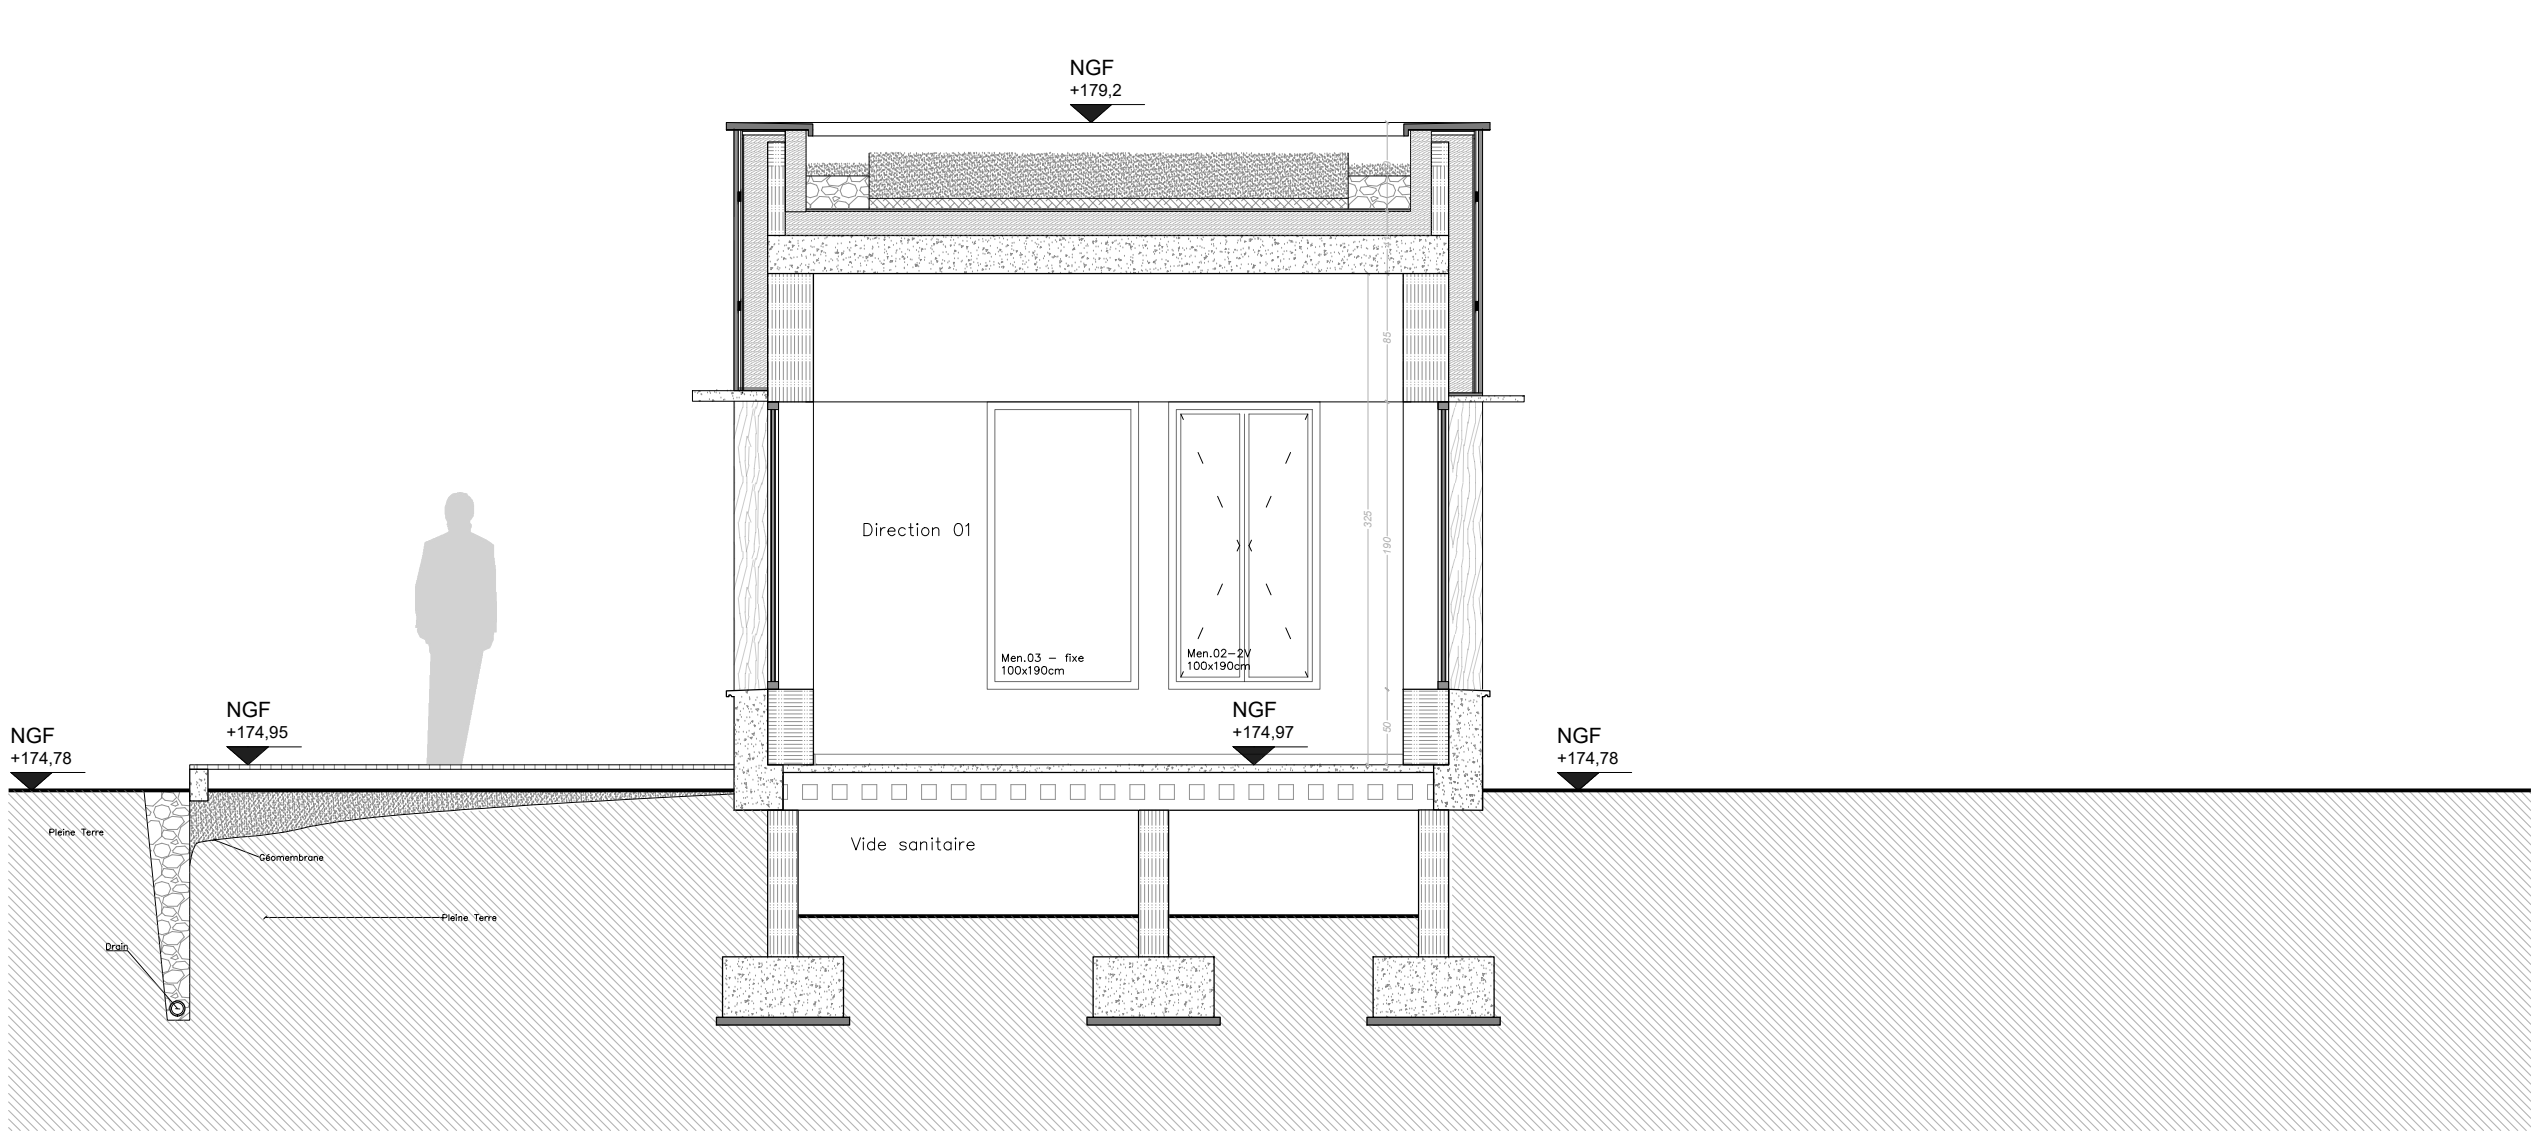


Coupe AA' – 1/100

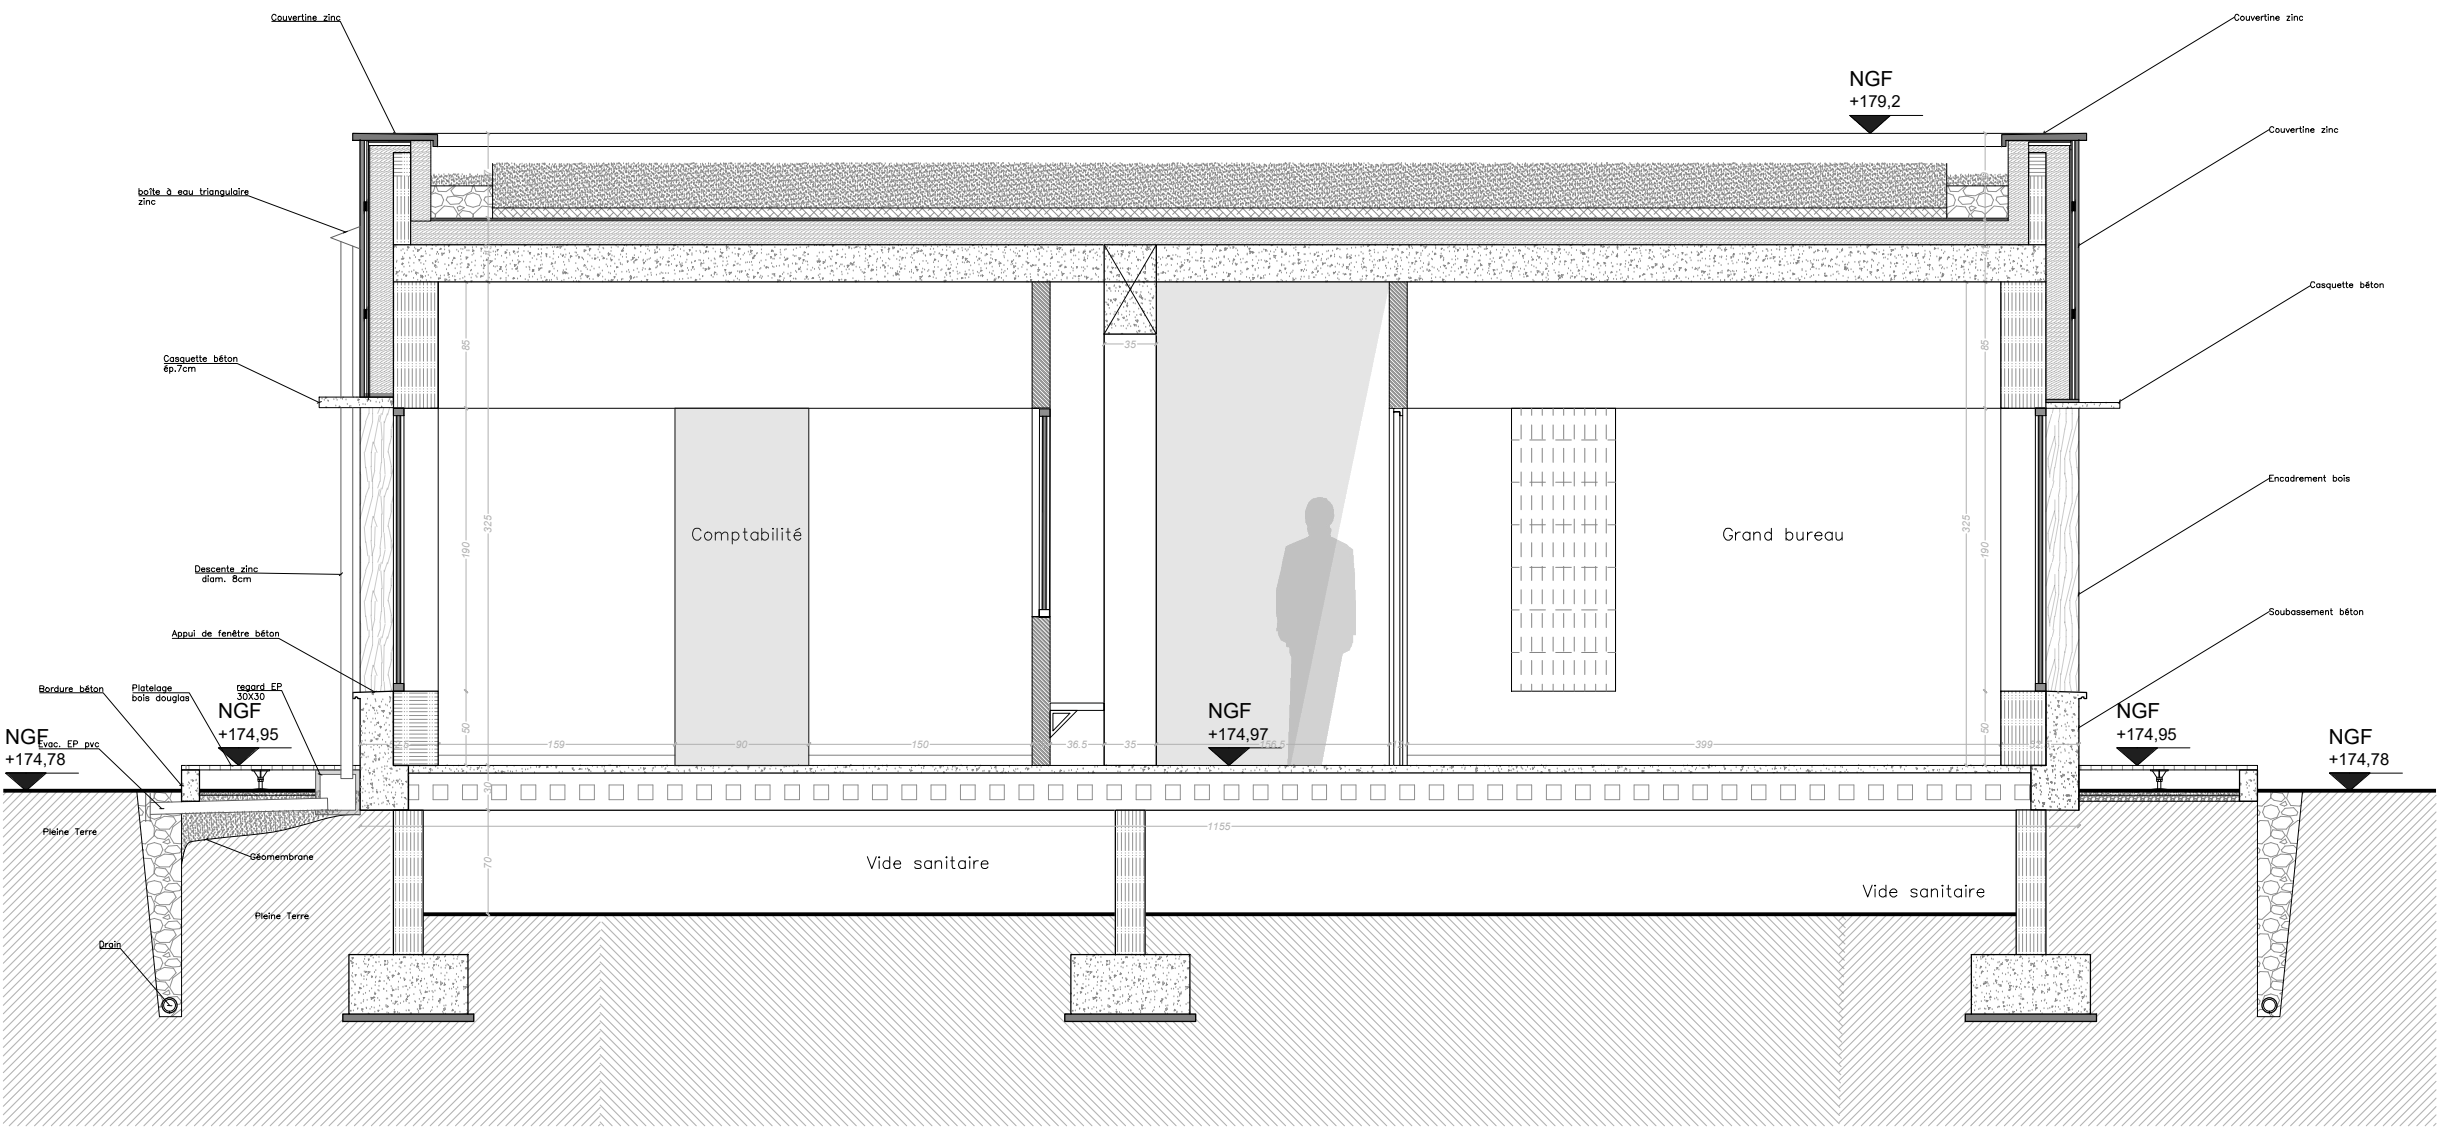


Coupe DD' – 1/100

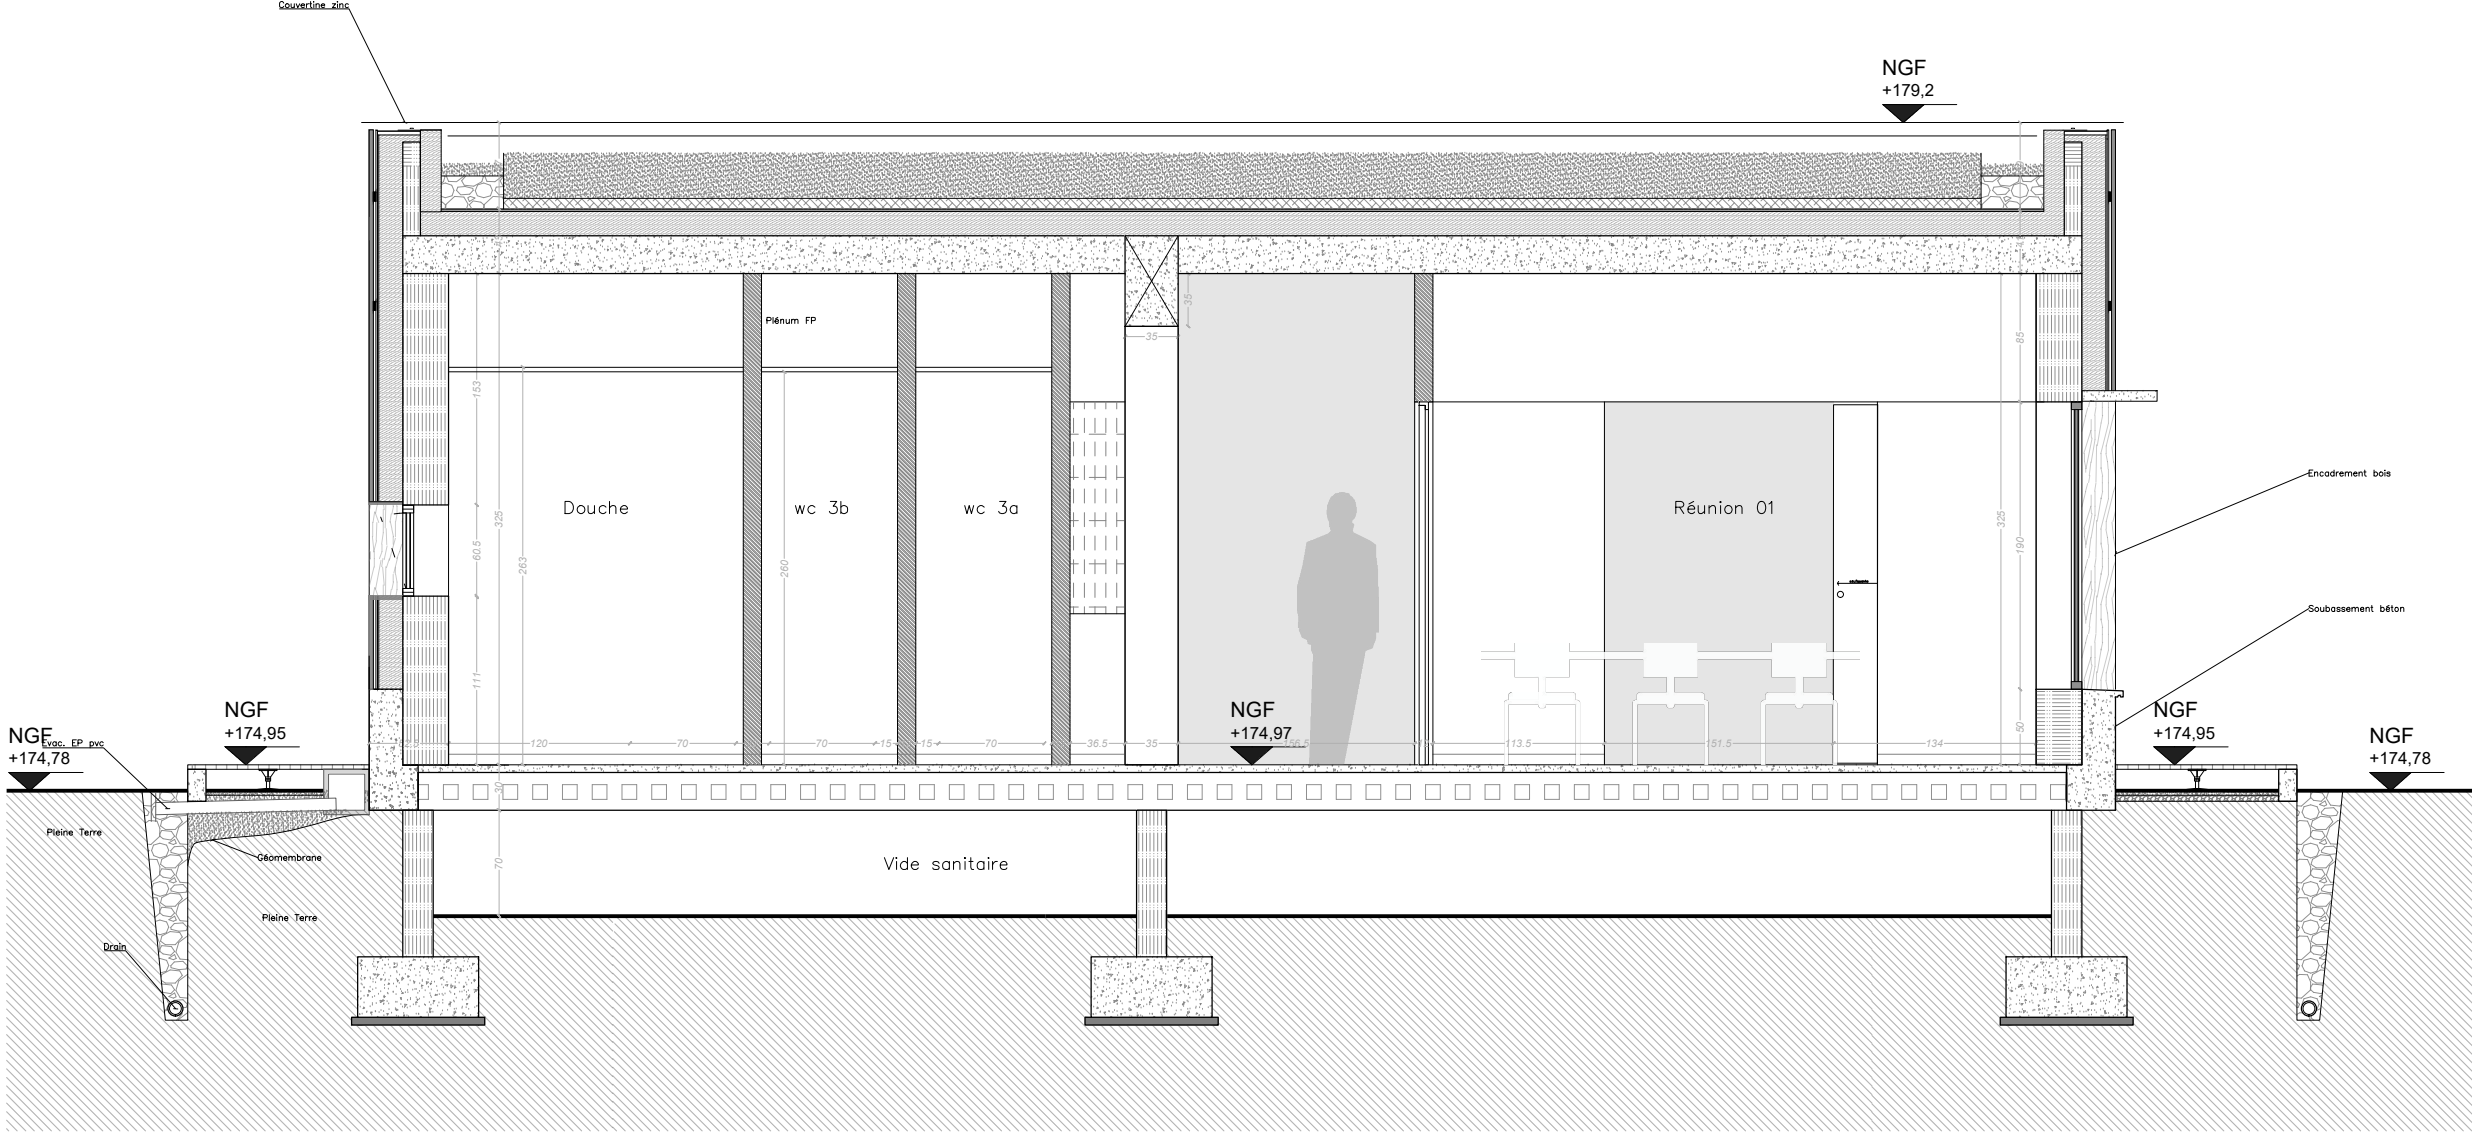


Coupe GG' – 1/100

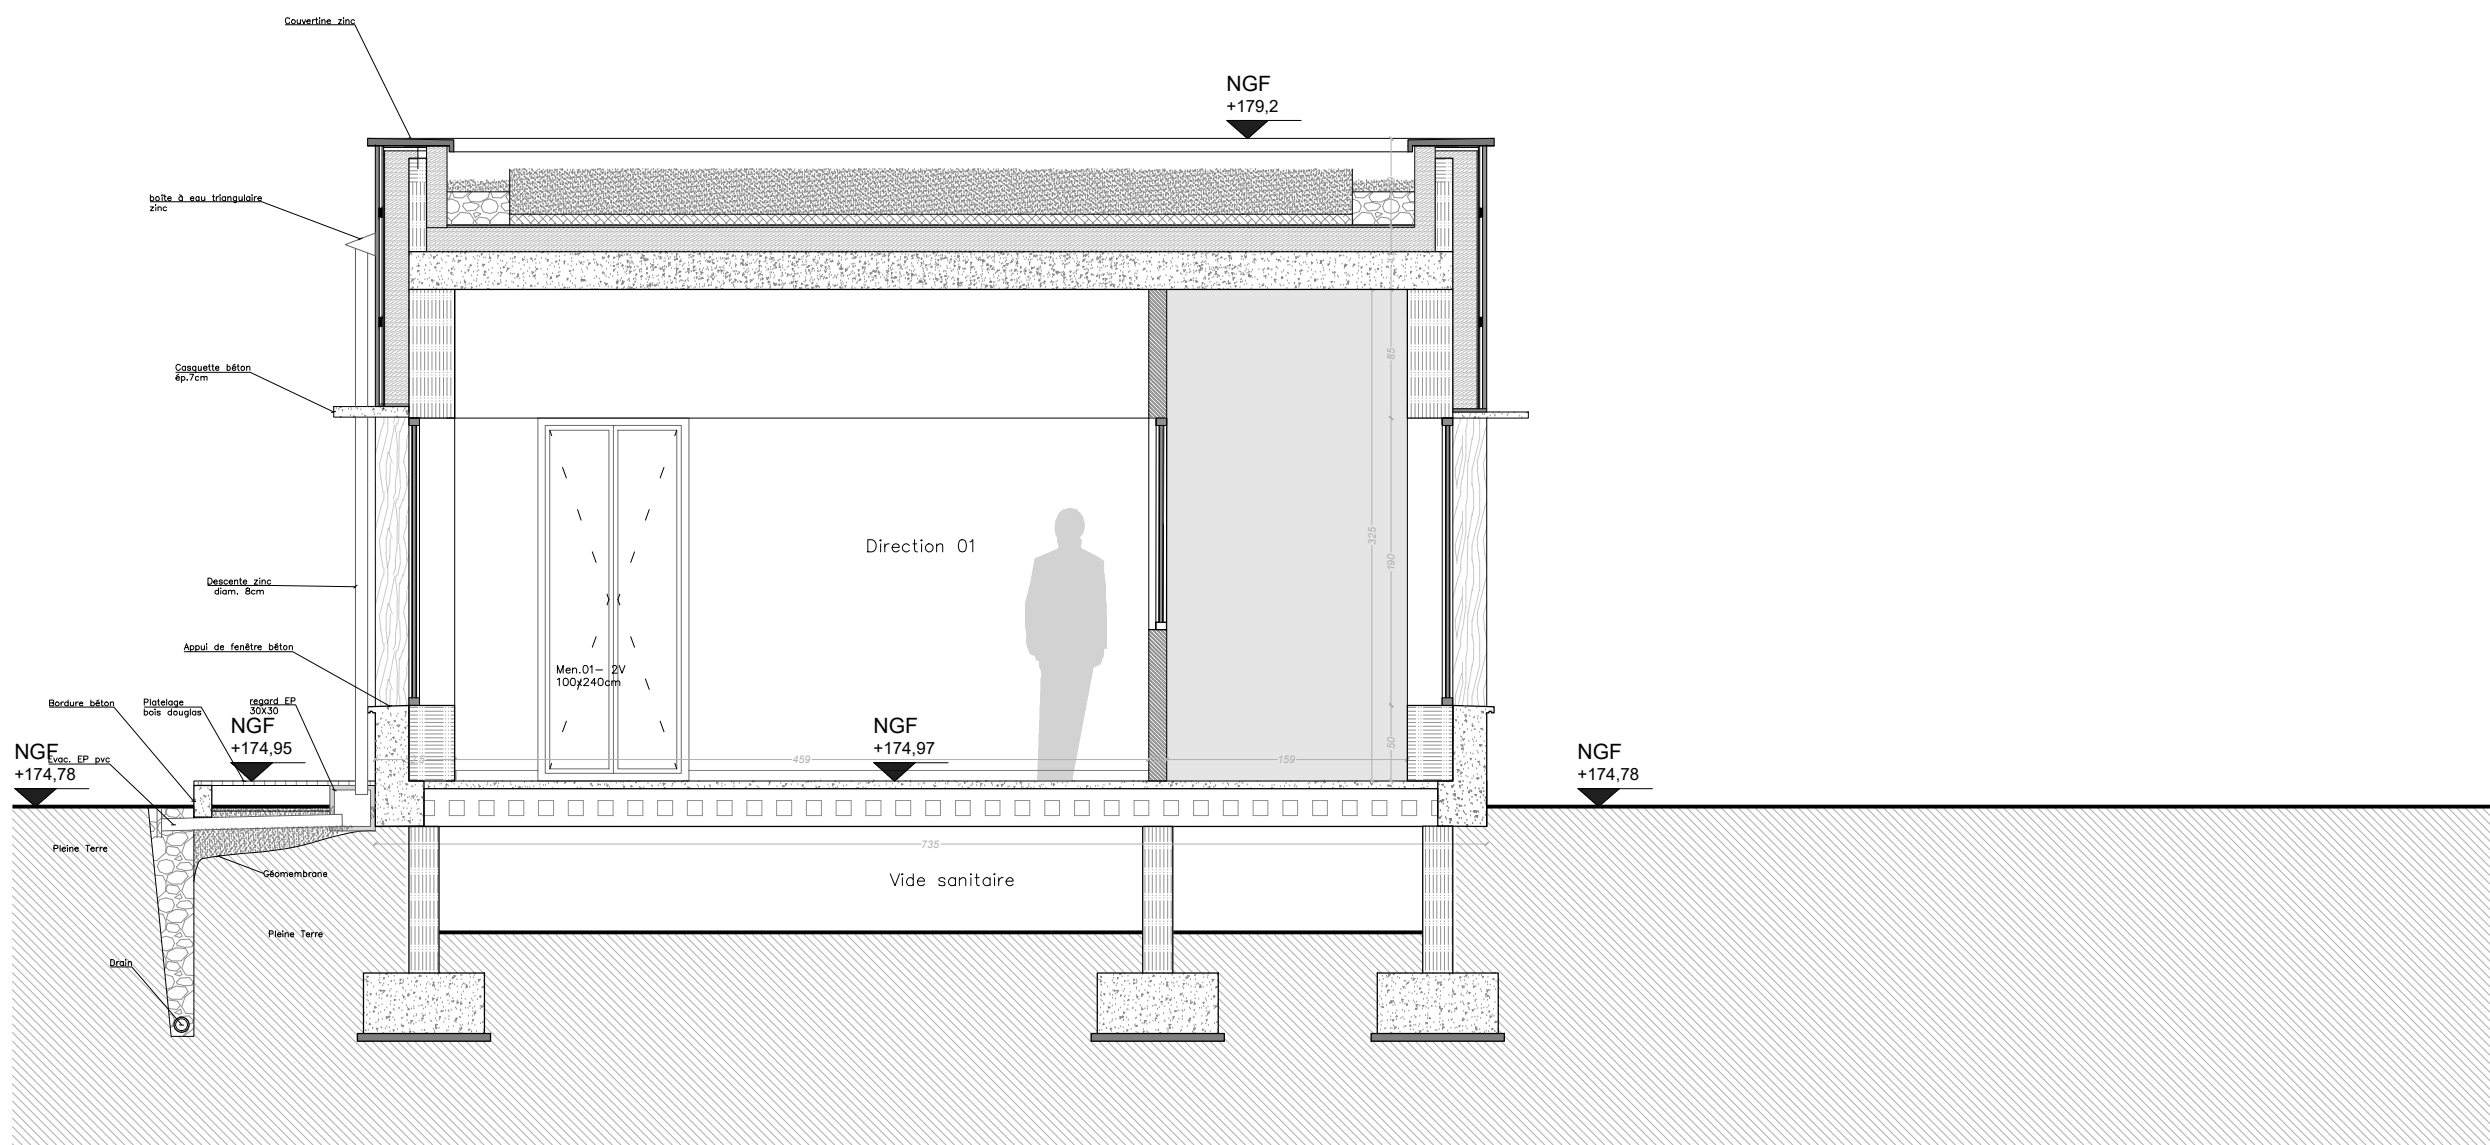


Coupe BB' – 1/100

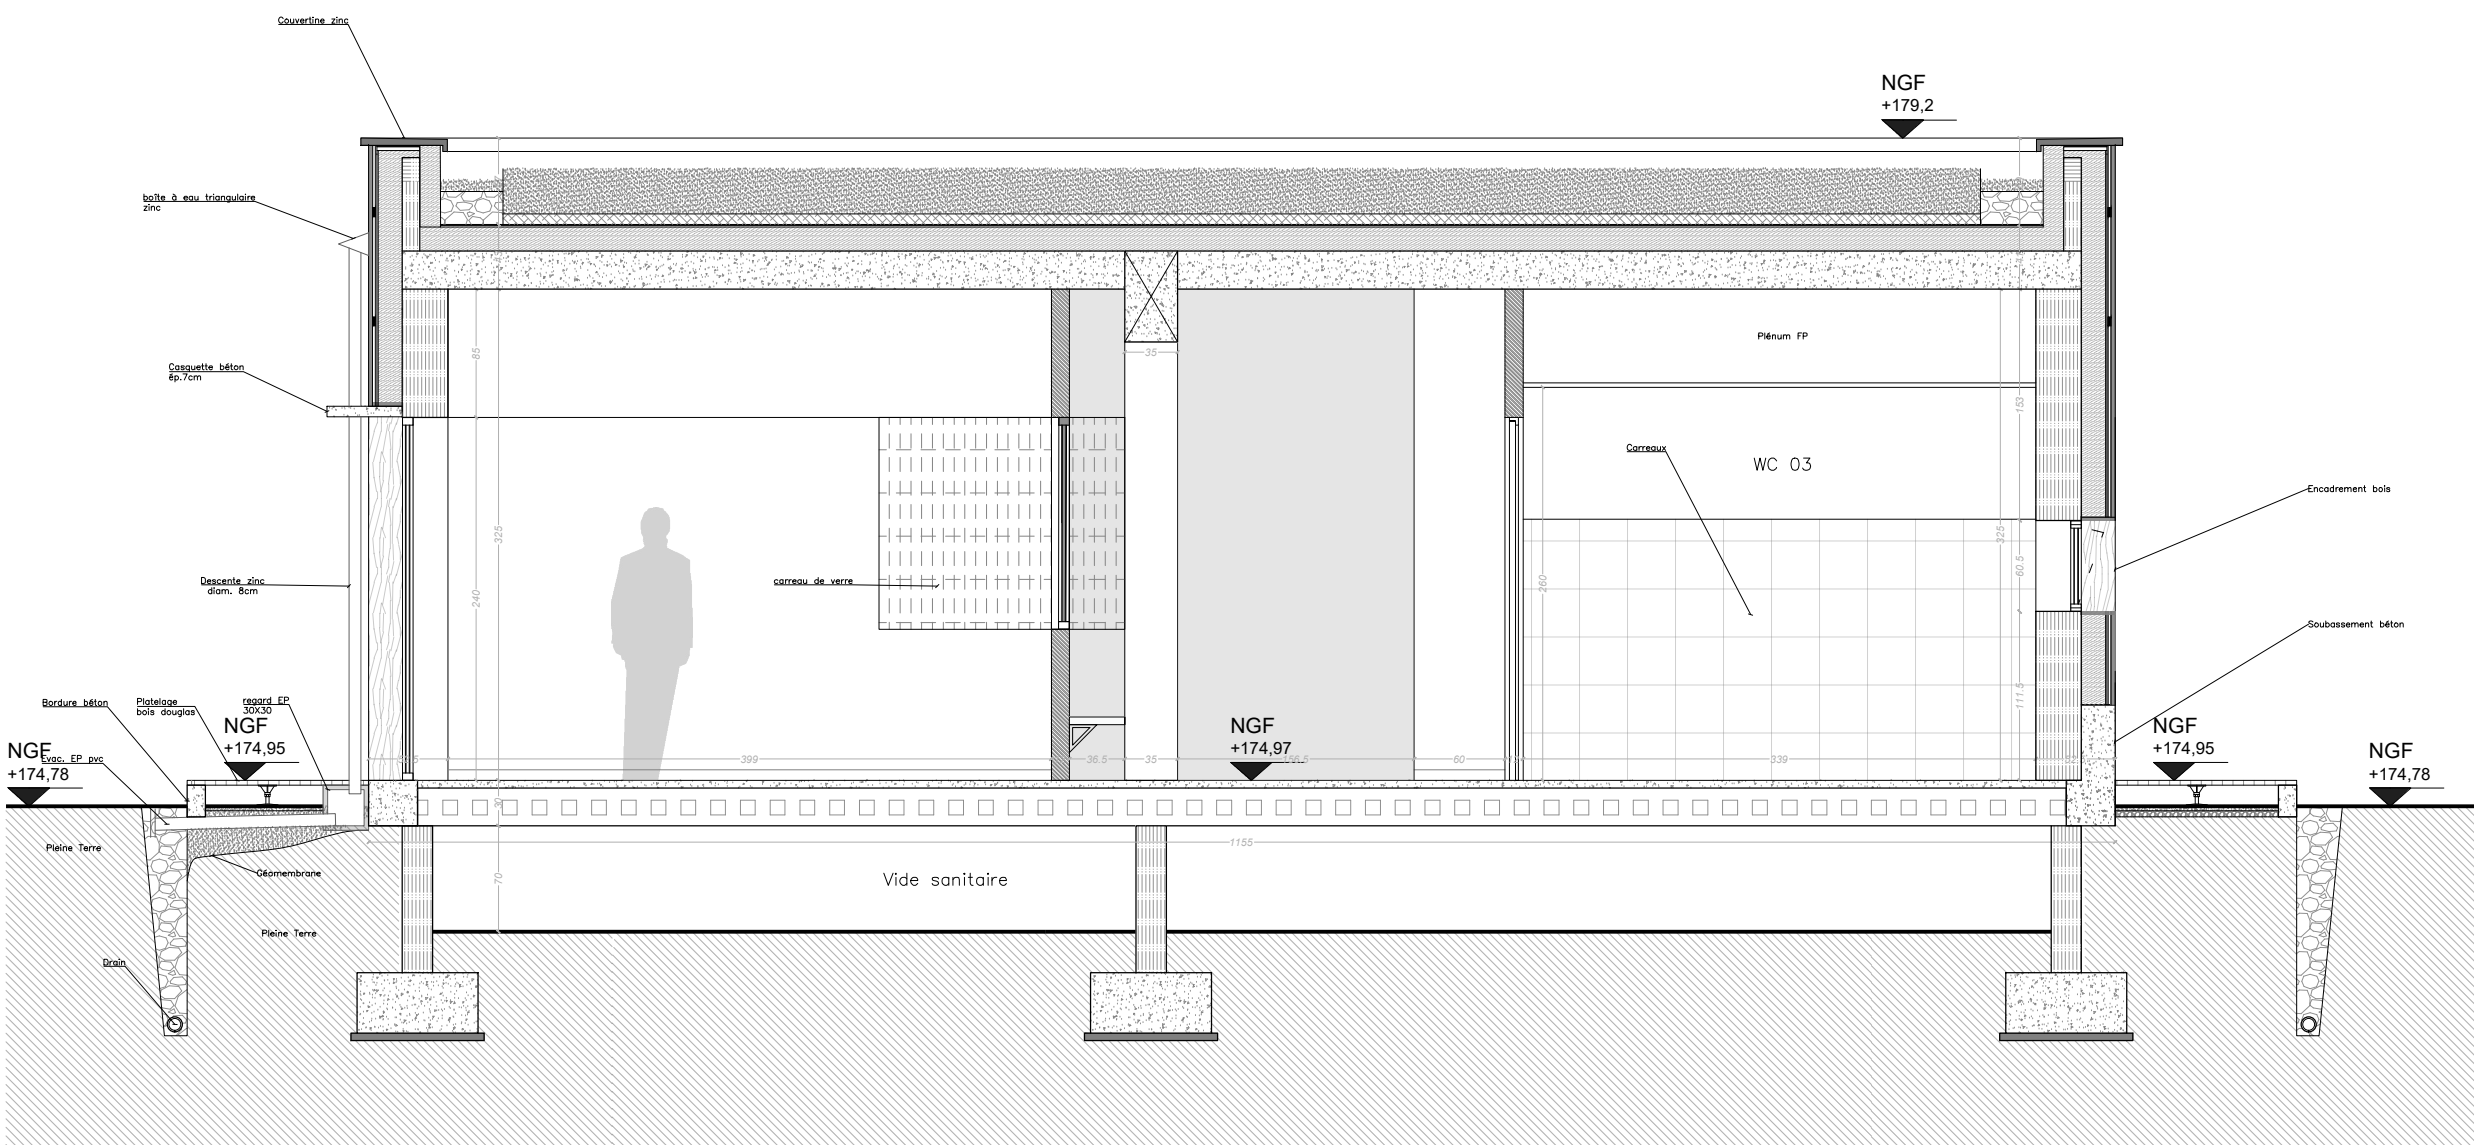


Coupe EE' – 1/100

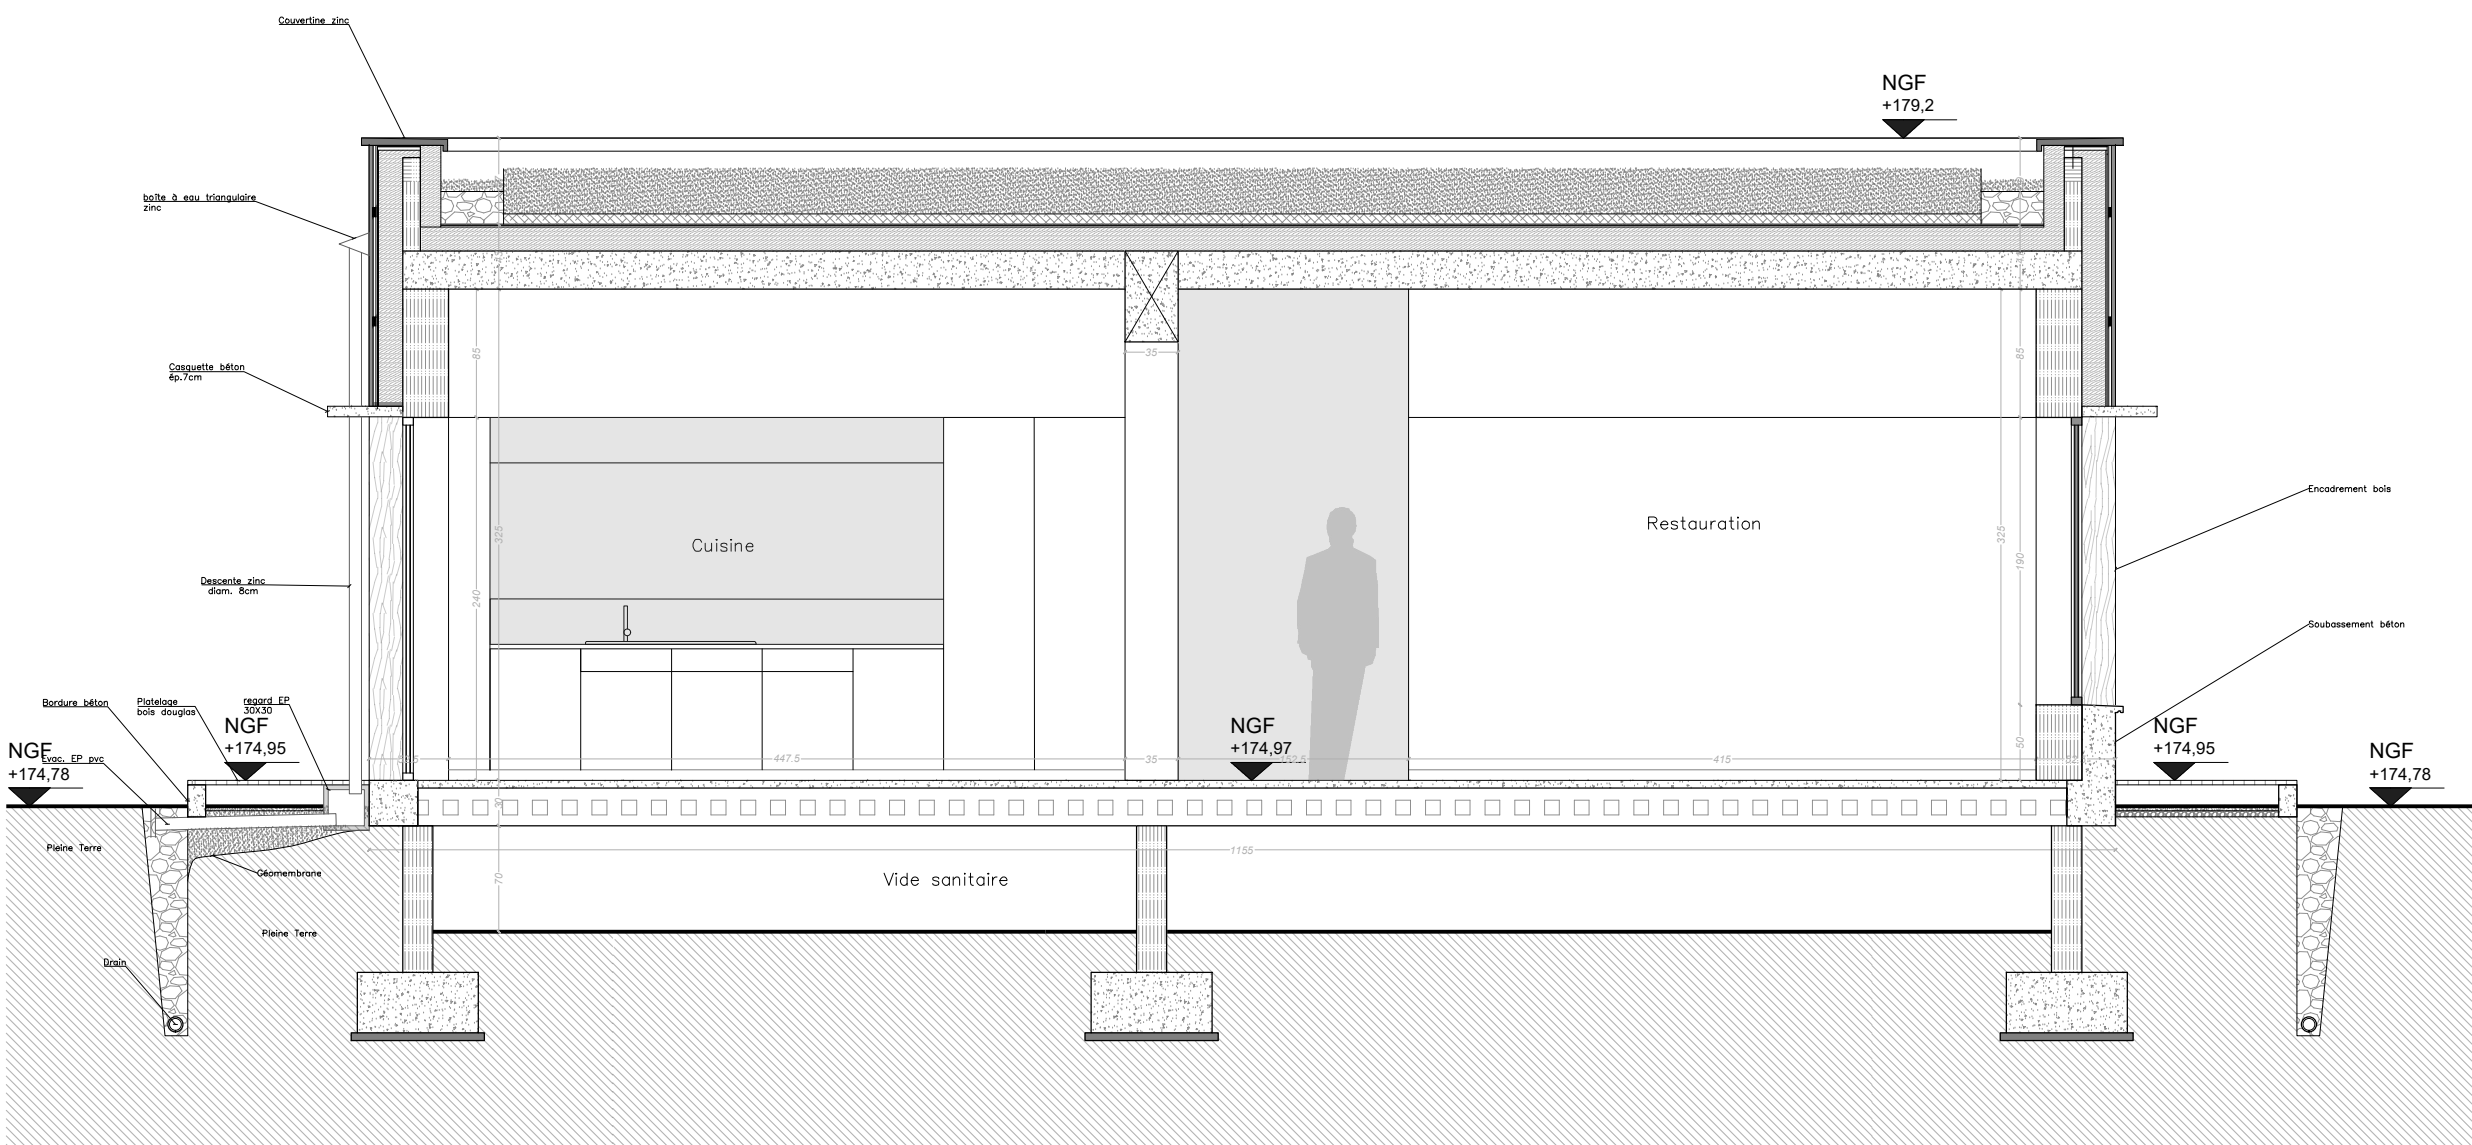


Coupe HH' – 1/100

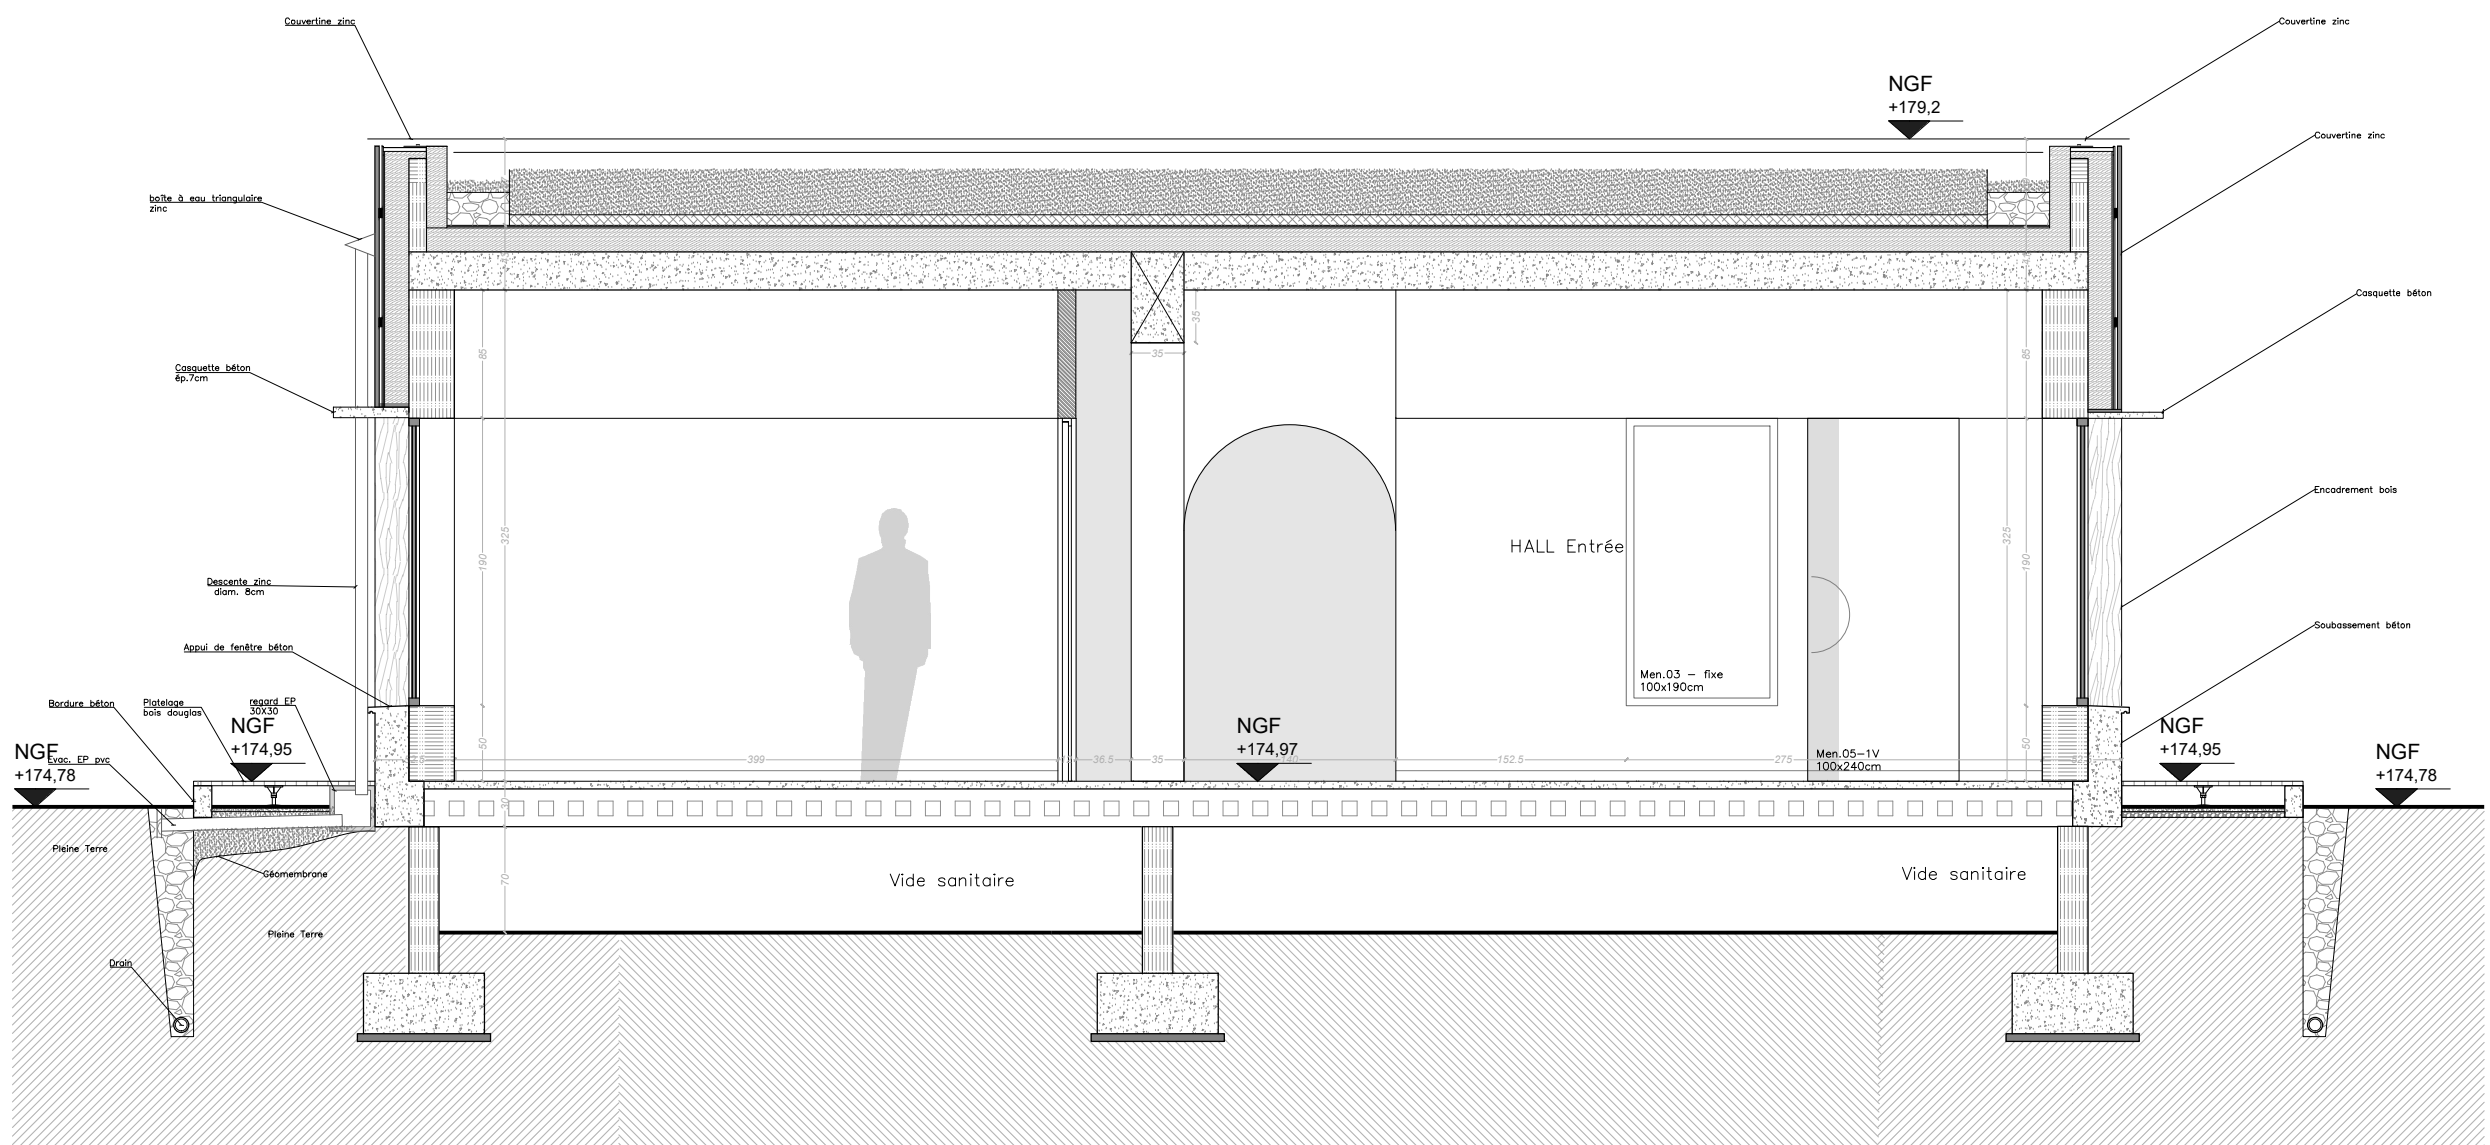

Coupe CC' – 1/100

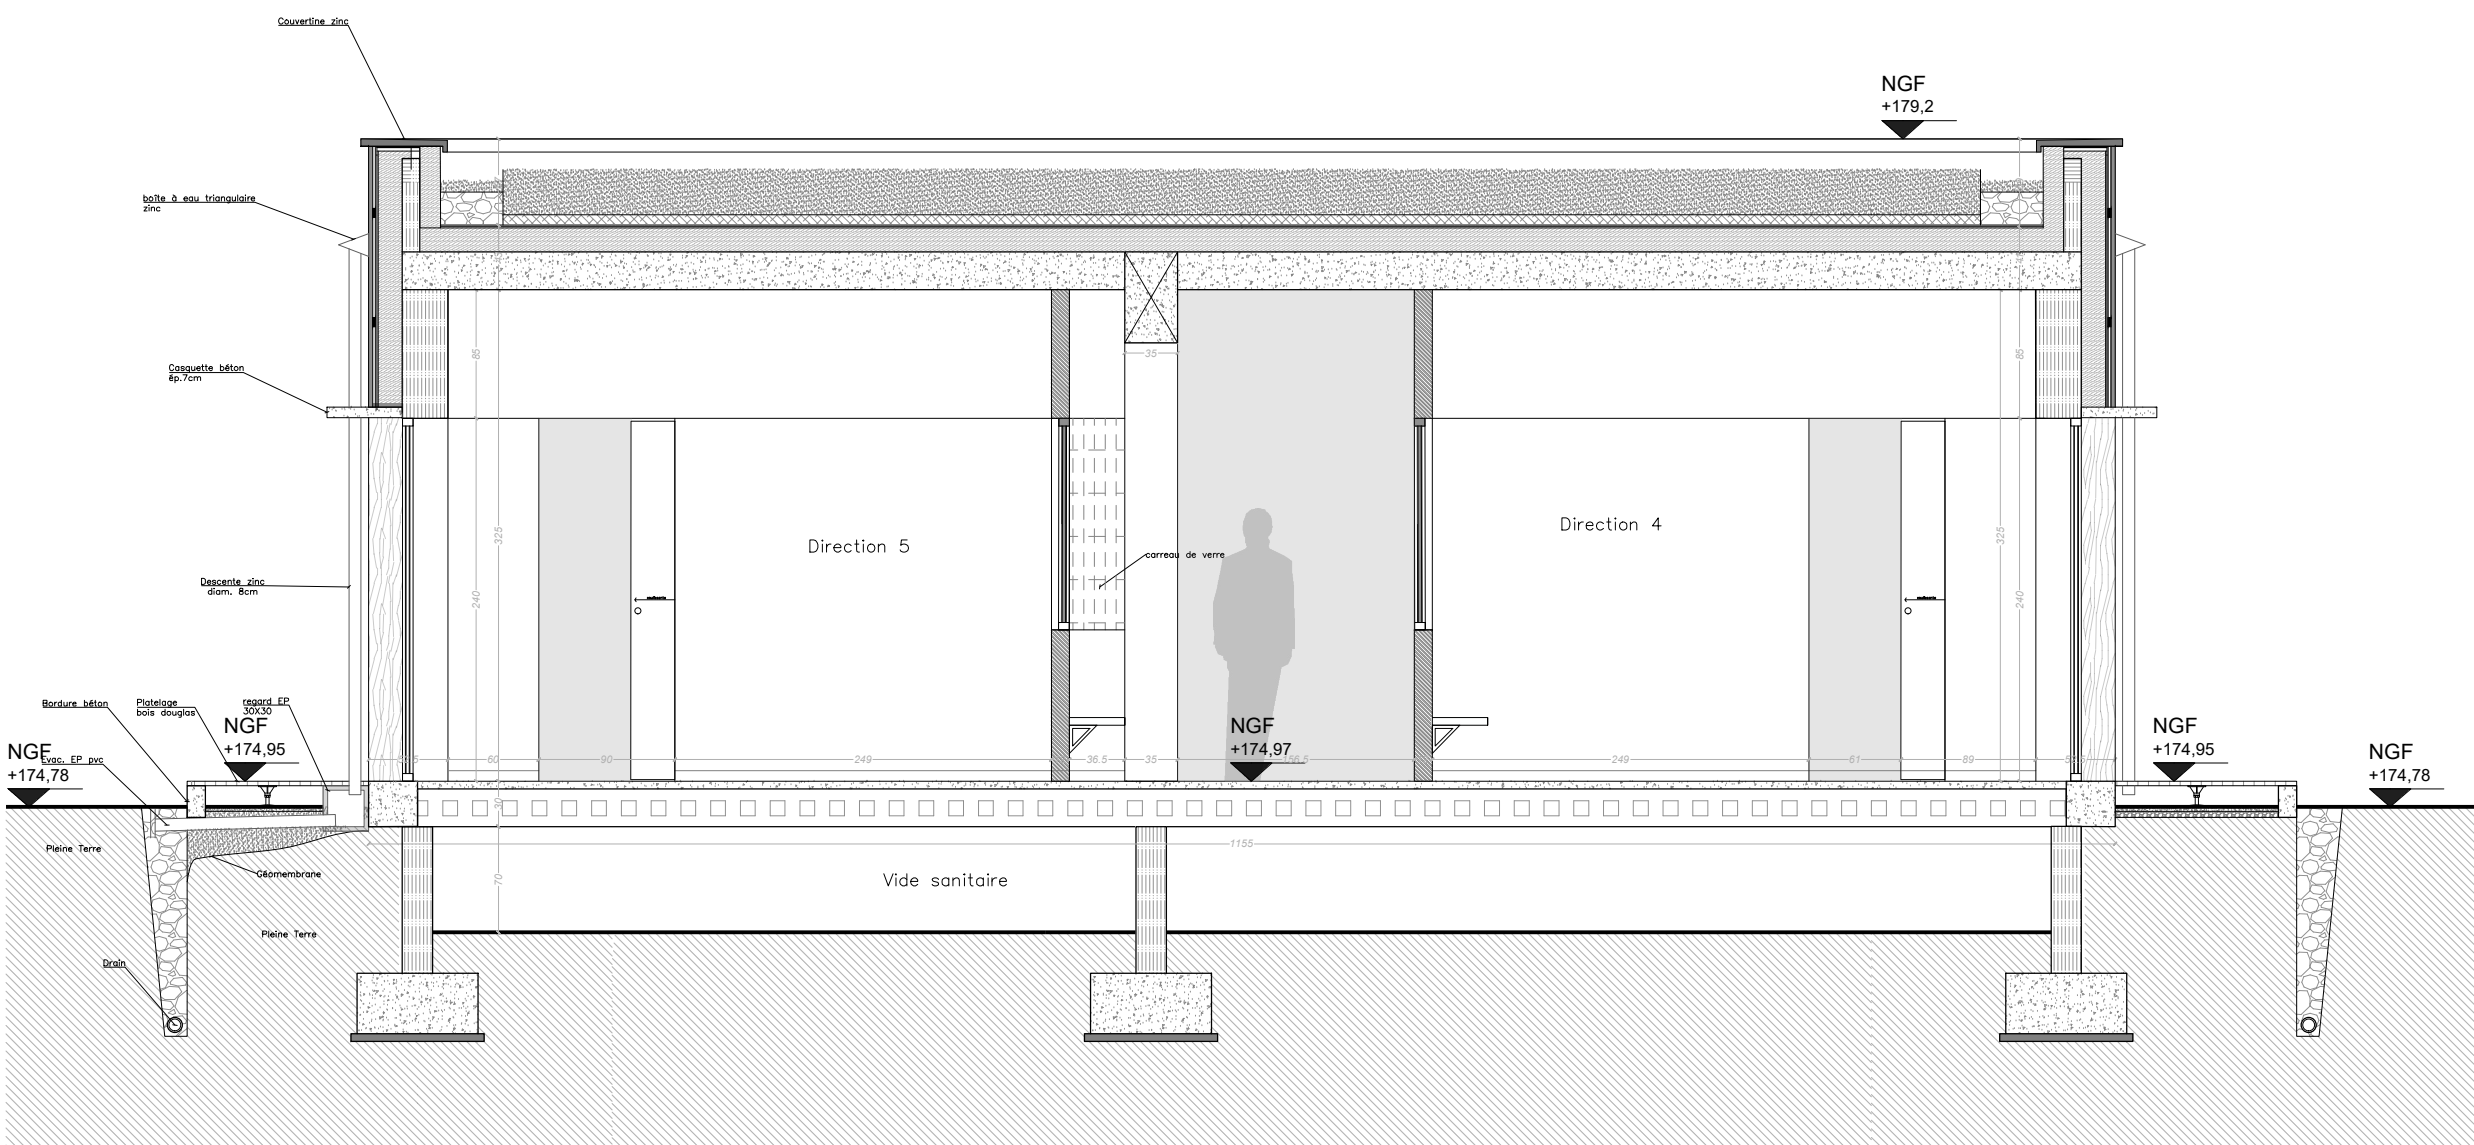

Coupe FF' – 1/100

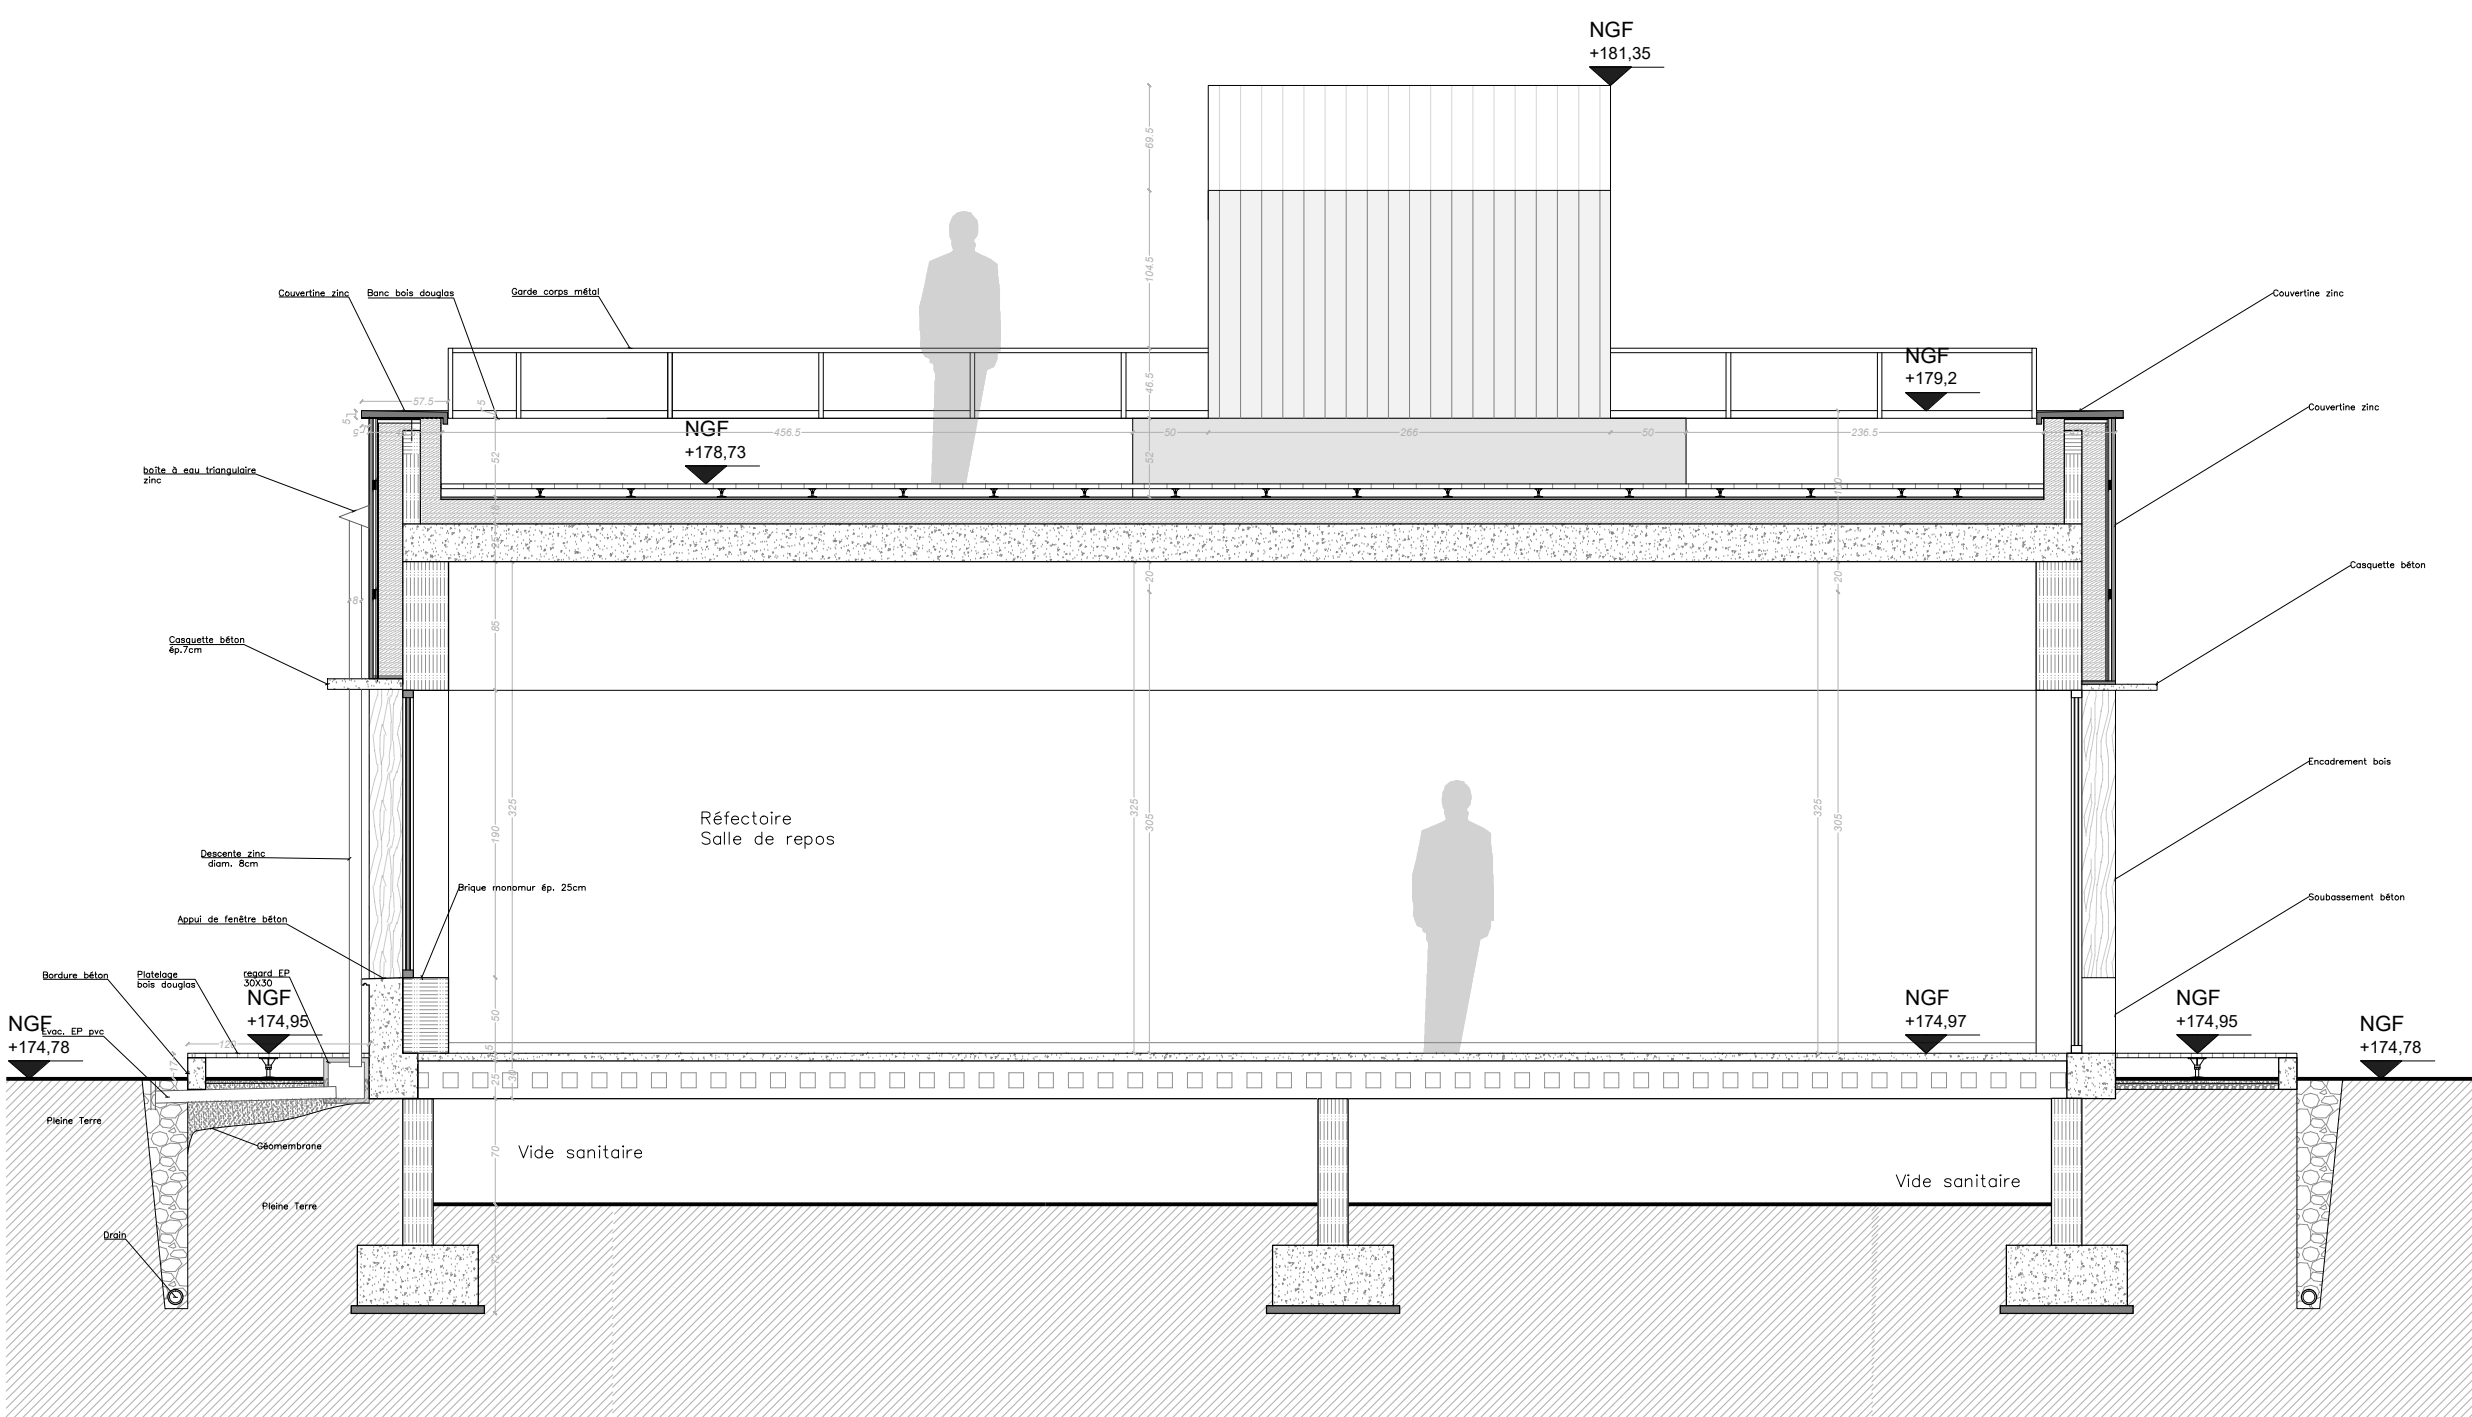

Coupe ii' – 1/100

MOE	MOA	PROJET	DOCUMENT	ECHELLE	LOT	FORMAT	DATE
MATHILDE LASSERRE – Architecte HMONP OÂ Ile-de-France – N°087975 63 Route de Rueil – 78150 – Le Chesnay lasserre.architecte@gmail.com +33680351075	ASSOCIATION LES TOUT PETITS Représentée par M.Legoff – Directeur Général 5 rue de Cernay – 91470 – Les Molières s.legoff@lestoutpetits.fr +33160121210	CONSTRUCTION DU SIEGE ADMINISTRATIF 1A allée de l'Orée du bois 91470 – Les Molières +33160121210	COUPES TRANSVERSALES	1/50	----	A0	04/12/2024